


МОНОЛИТНАЯ П-ОБРАЗНАЯ ЛЕСТНИЦА


M 1:10

План разбивки ступеней по линии движения

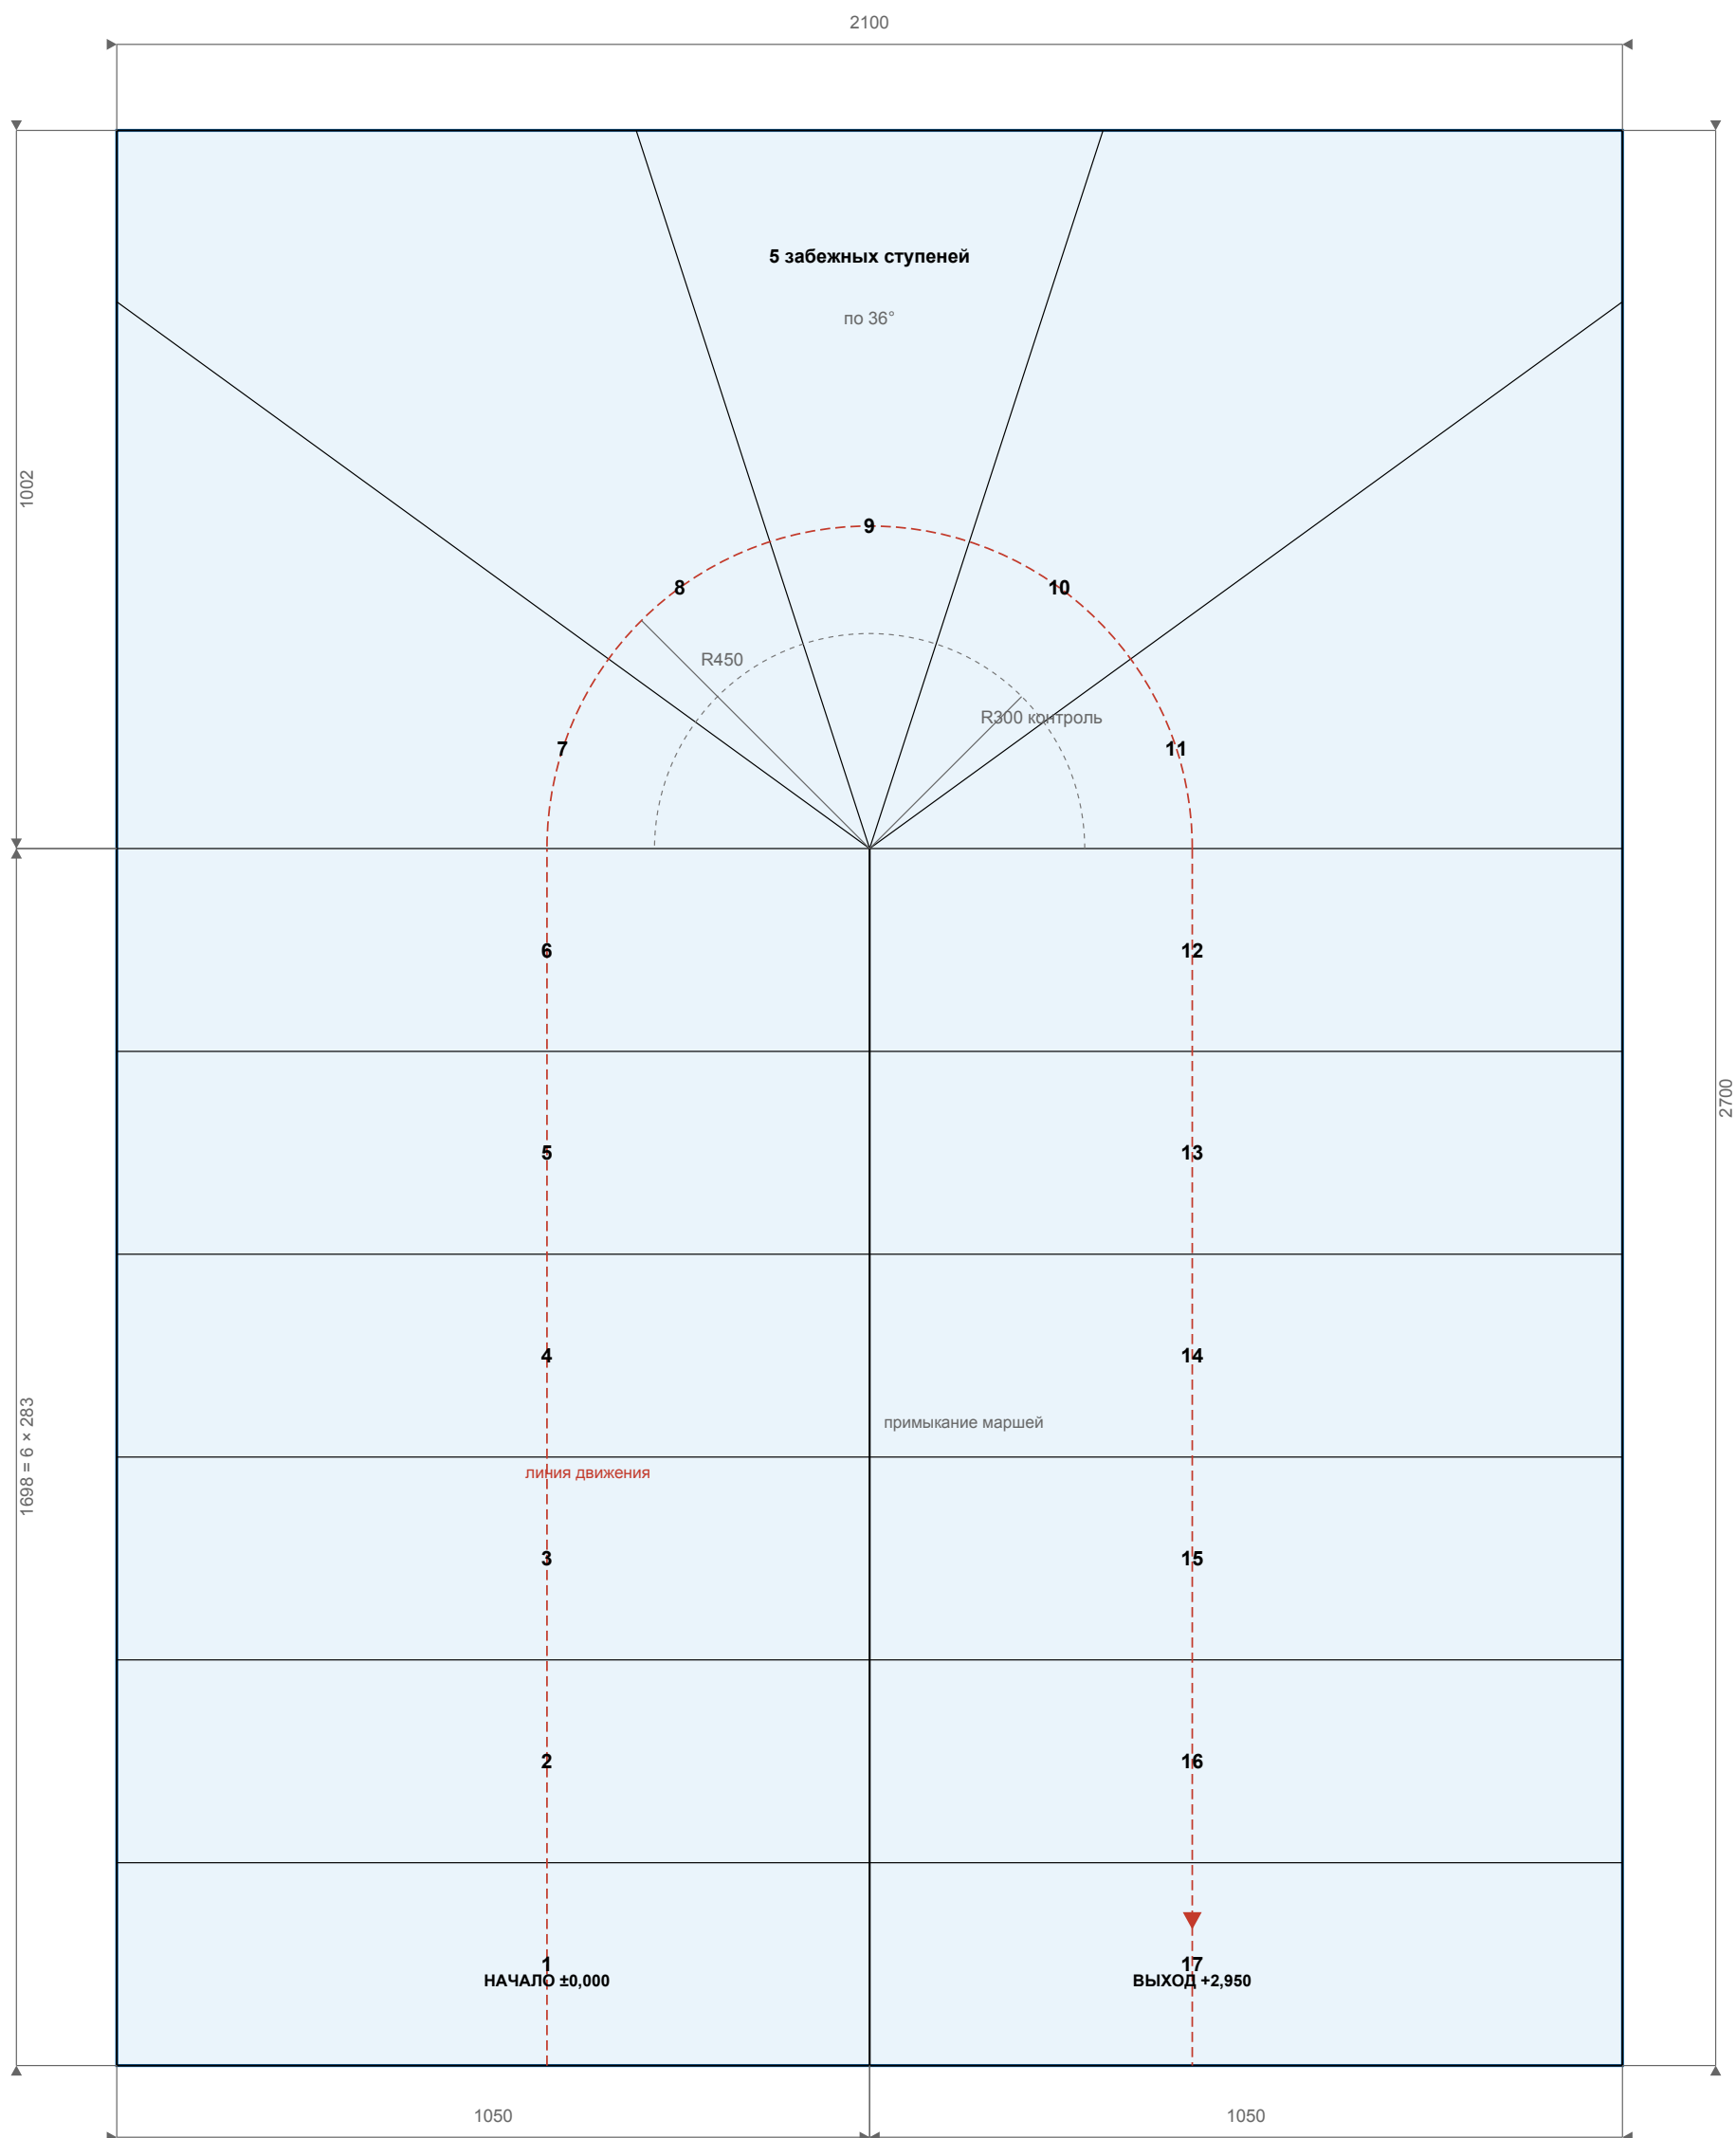

План лестницы и разбивка забежных ступеней	Масштаб 1:10	
Геометрическая рабочая схема. Раздел АР	Лист 1 / 2	05.09.2026
Проём 2100 × 2700. Перепад чистых полов 2950. Марши без просвета.	Перед бетонированием сверить чистые отметки	

Все 18 подступенков одинаковые после чистовой отделки

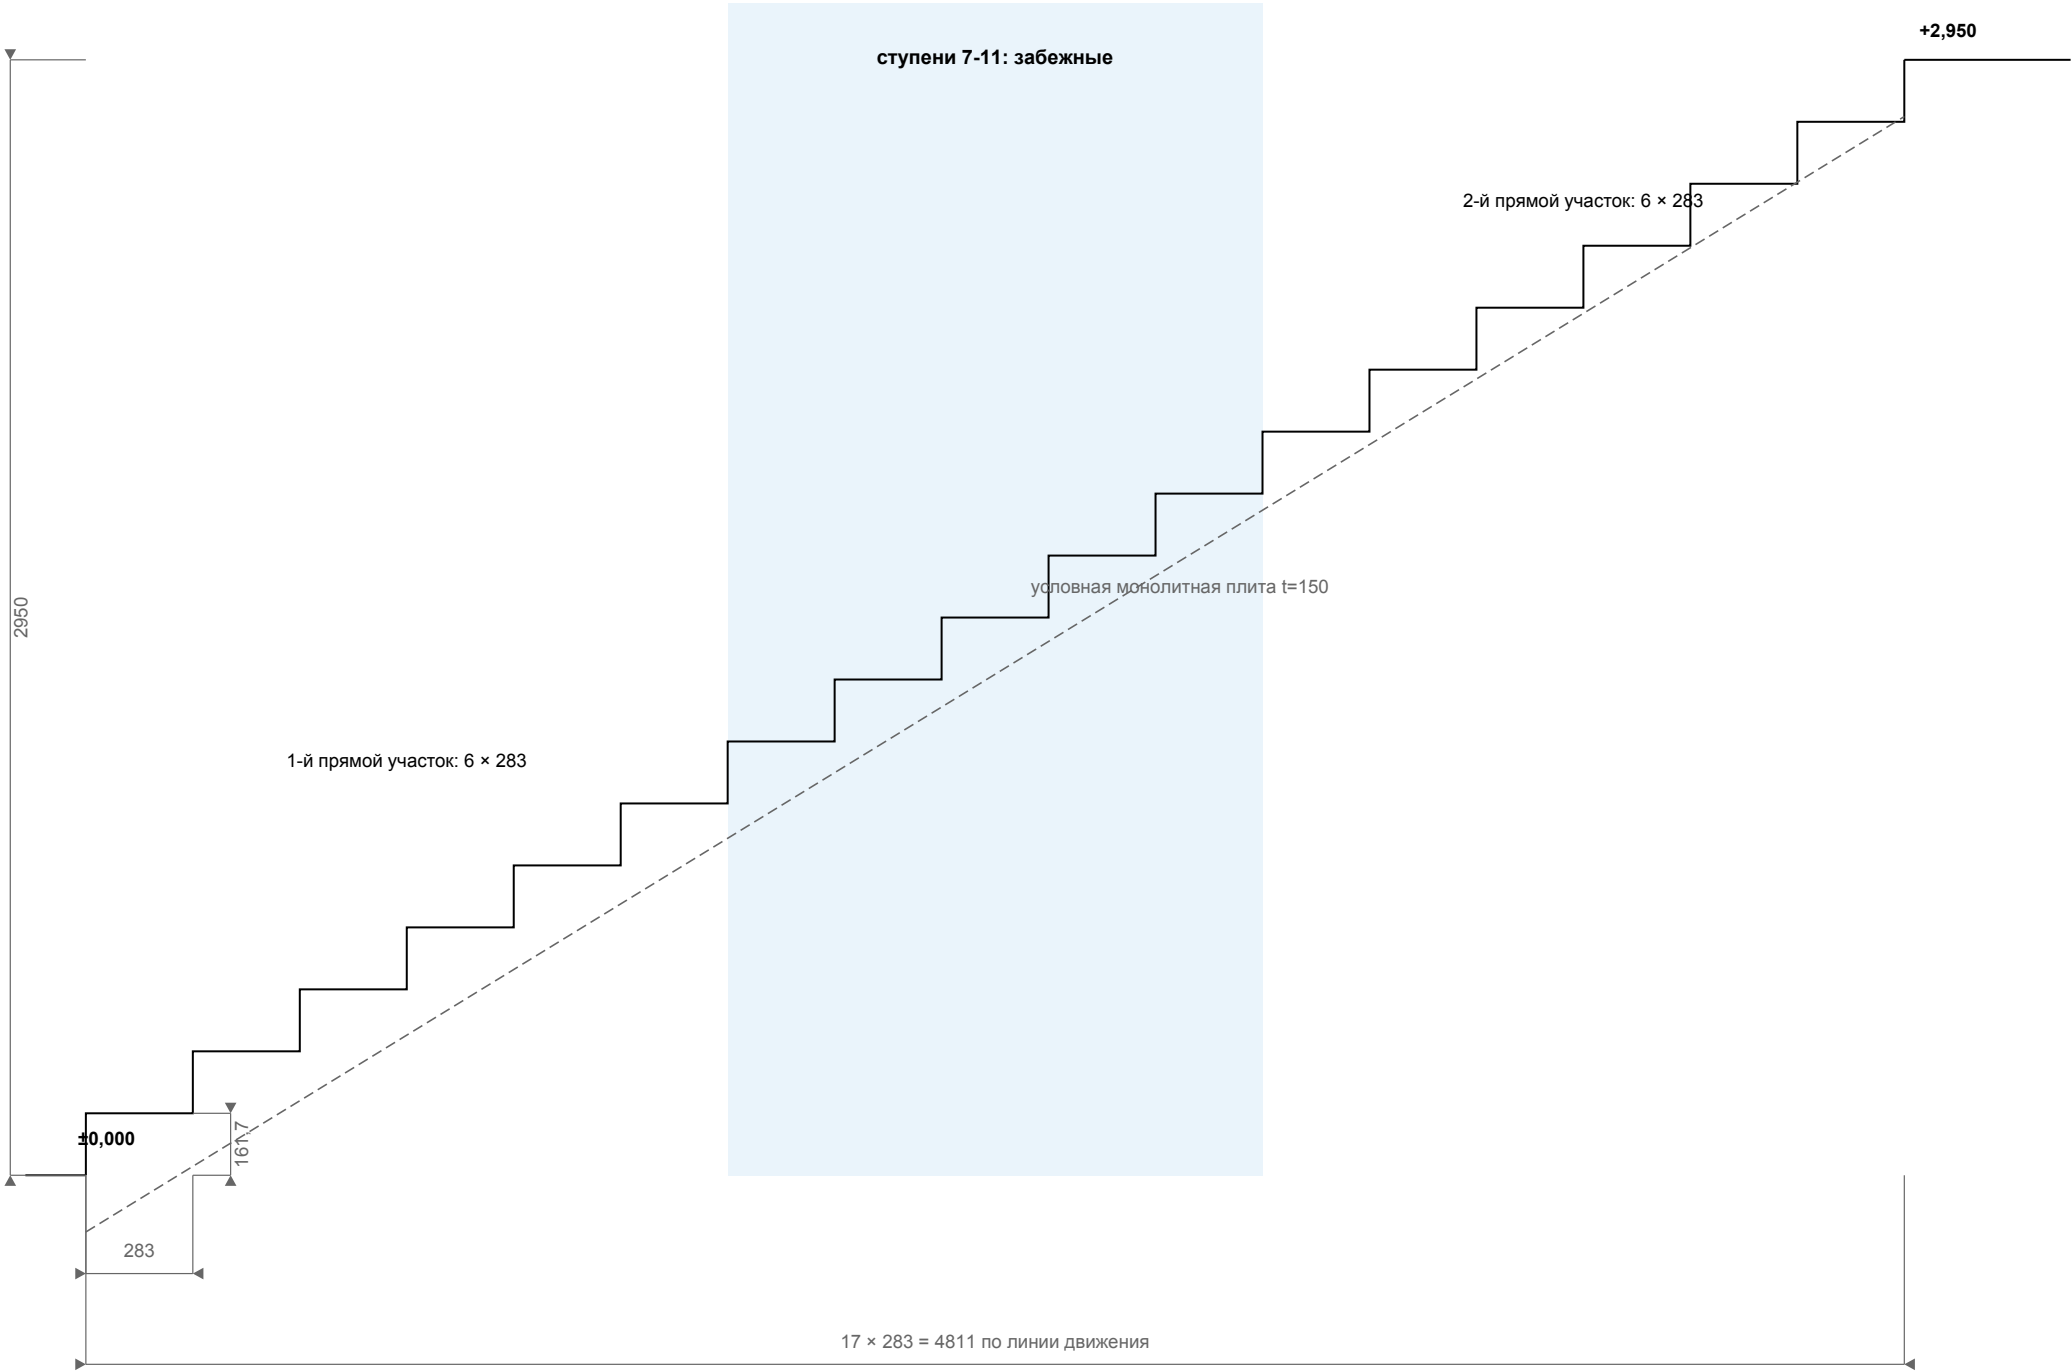

КОНТРОЛЬНЫЕ ПАРАМЕТРЫ	
Высота между чистыми полами	2950 мм
Количество подъёмов	18
Подступенок h	163,9 мм
Проступь b	283 мм
Разбивка	6 + 5 + 6
Ширина каждого марша	1050 мм
Просвет между маршами	0 мм
Радиус линии движения	450 мм
Шаг забежной по линии	282,7 мм
Шаг на контрольной R300	188,5 мм
Угол одной забежной	36°
2h + b	610,8 мм
Уклон прямого участка	30,1°

ПРИМЕЧАНИЯ

- Размеры даны по чистовым поверхностям и чистым уровням пола.
- Марши примыкают друг к другу по центральной оси. Просвет и разделительная стенка не предусматриваются.
- Границы пяти забежных ступеней заданы радиально через 36°. На линии движения R450 шаг составляет 282,7 мм, на контрольной линии R300 - 188,5 мм.
- Перед изготовлением опалубки выполнить контрольный замер фактического проёма и отметок обоих полов.
- Толщина плиты t=150 показана условно. Армирование, опирание и фактическую толщину назначает конструктор раздела ЮК.
- Проверить высоту прохода по всей линии движения после учёта толщины перекрытия и отделки.
- Ограждения, закладные детали и узлы примыкания разрабатываются отдельными чертежами.

Развёртка и контрольные параметры		Масштаб 1:20	
Геометрическая рабочая схема. Раздел АР		Лист 2 / 2	05.09.2026
Проём 2100 × 2700. Перепад чистых полов 2950. Марши без просвета.		Перед бетонированием сверить чистые отметки	