



МОНОЛИТНАЯ П-ОБРАЗНАЯ ЛЕСТНИЦА. АРМИРОВАНИЕ

Схема выполнена по геометрии проёма 2100 x 2700 мм и по структуре загруженного образца

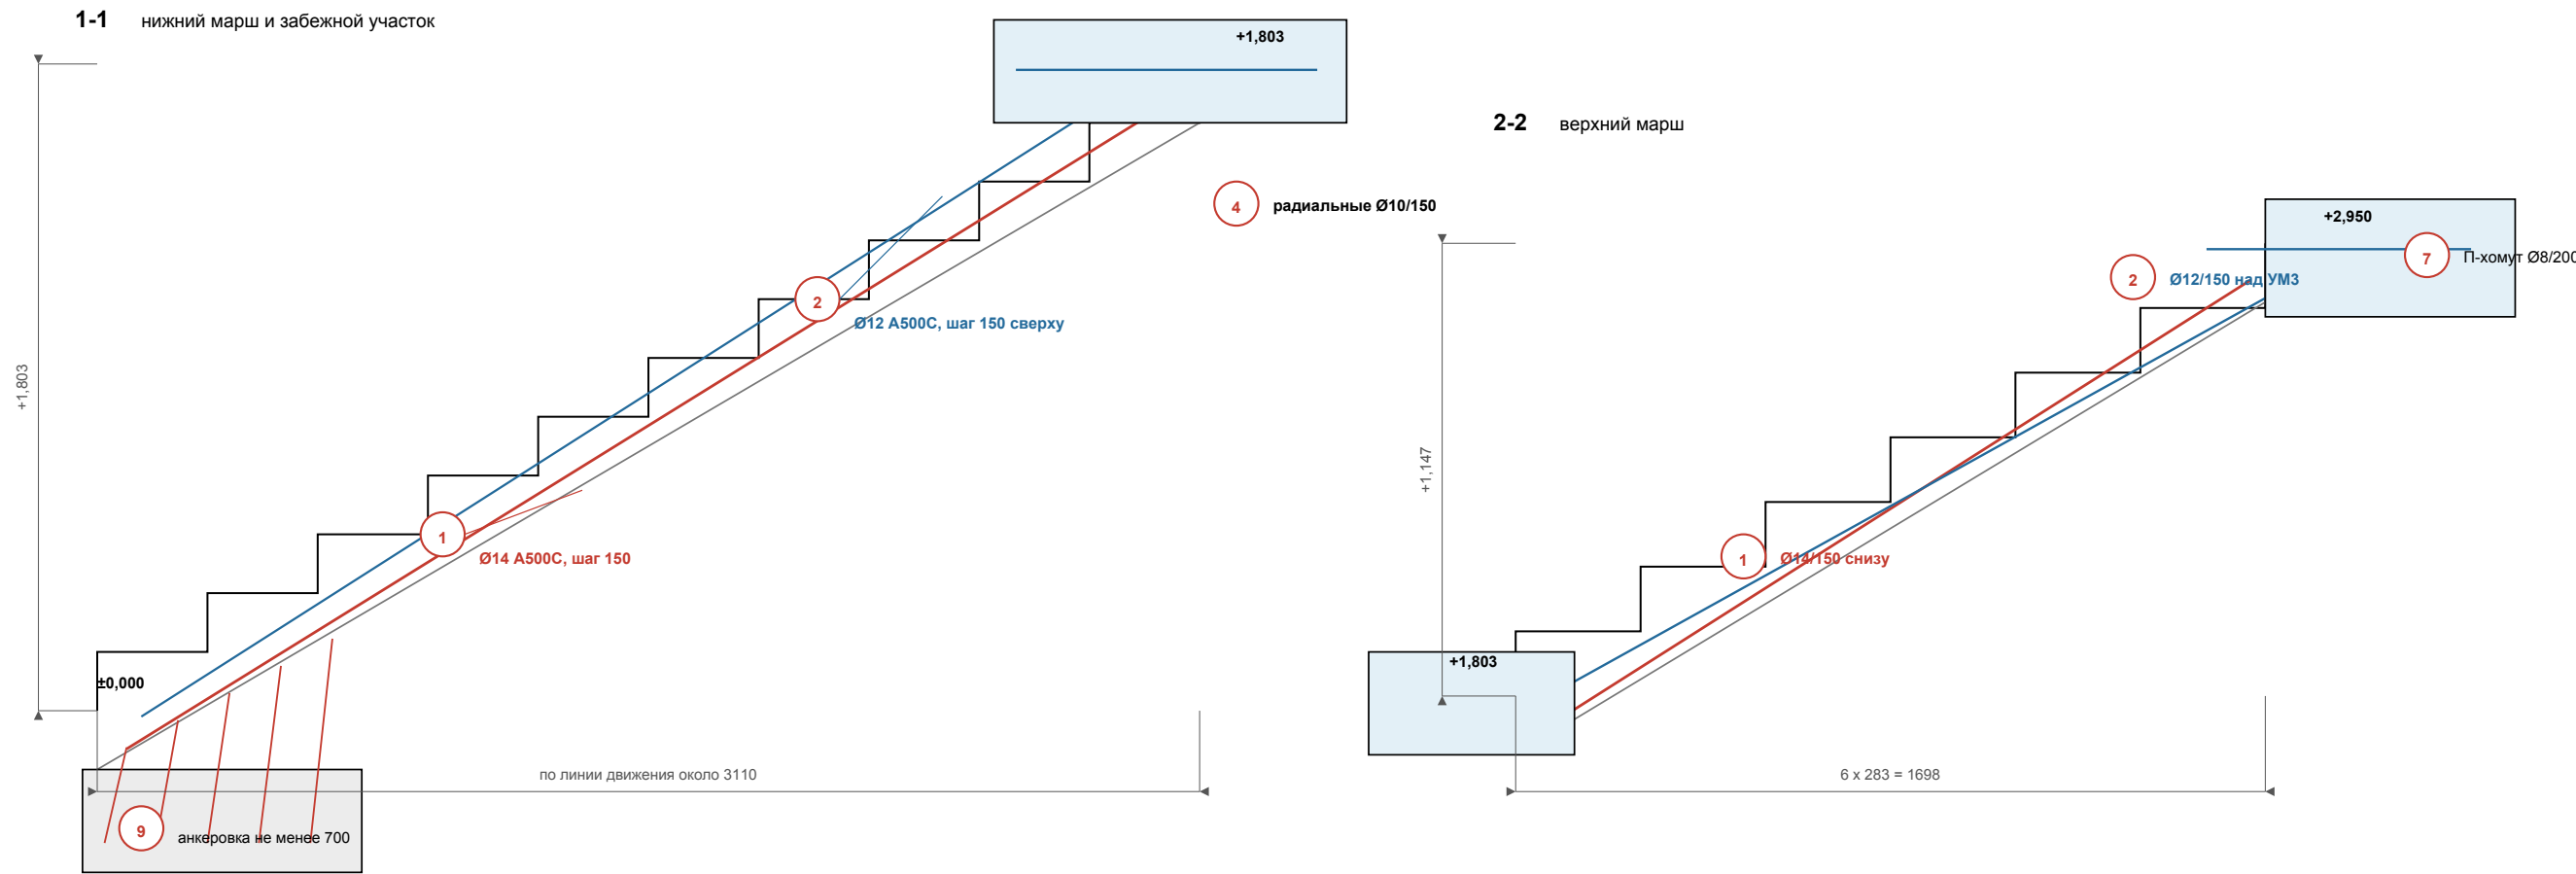


Плита марша t=160 мм по нормали; защитный слой 25 мм. Все пересечения арматуры вязать.

ПЛАН ЗАБЕЖНОГО УЗЛА

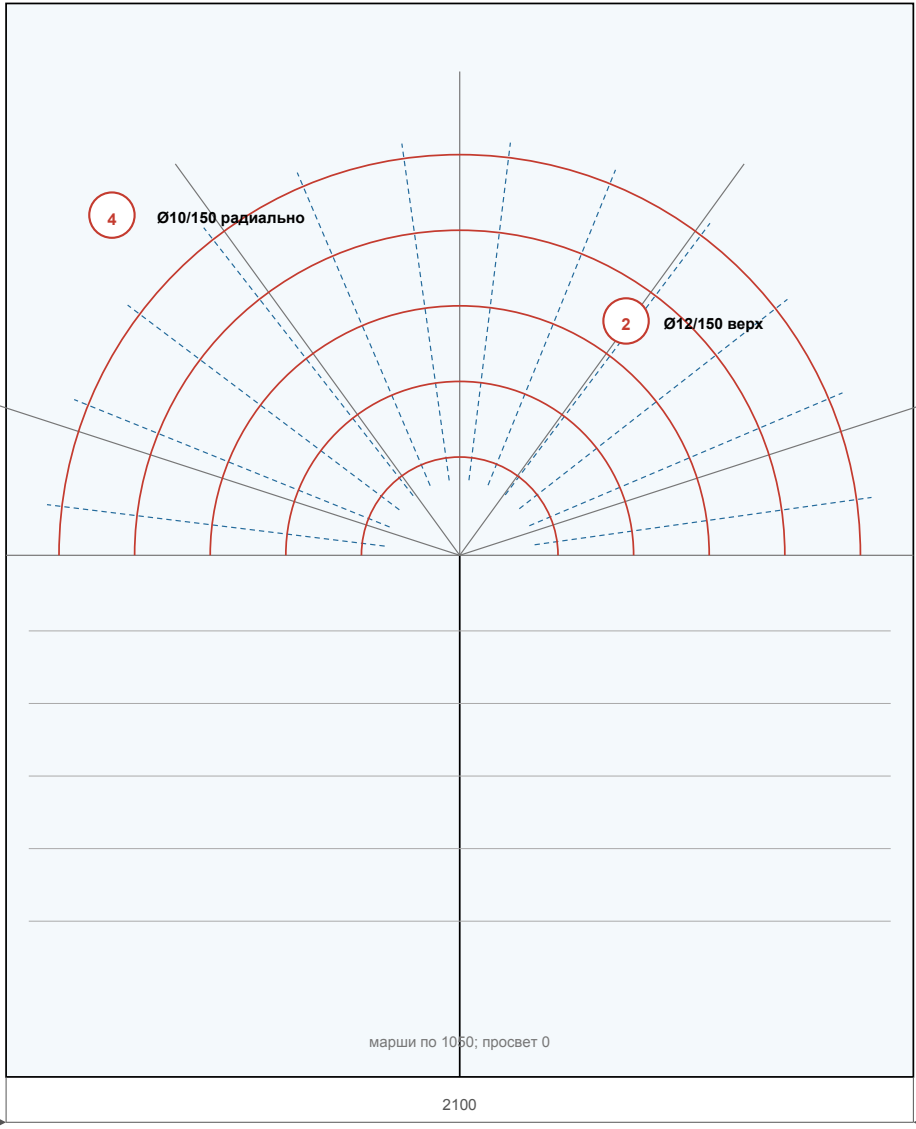


СЕЧЕНИЕ МАРША А-А

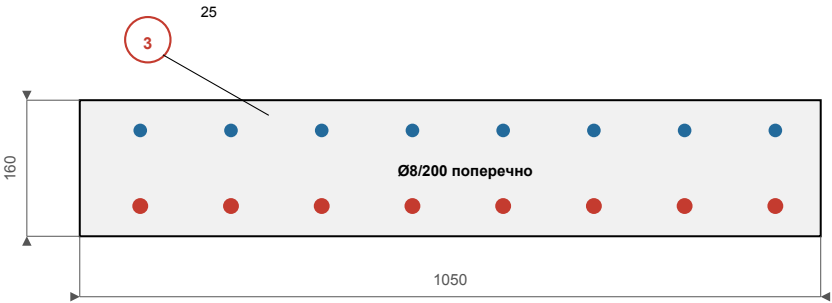

ОБЩИЕ УКАЗАНИЯ

- Бетон лестницы - В25 (С25/30), арматура - А500С. Толщина плиты марша 160 мм.
- Рабочую арматуру не обрывать в вершине забежных ступеней; забежный узел бетонировать без рабочего шва.
- Верхнее опирание выполнить в монолитный участок УМЗ t=220 мм; выпуски Ø14/150 завести не менее чем на 700 мм.
- Нижнее опирание допускается только на несущую железобетонную плиту или фундамент, но не на стяжку пола.
- Длины и количество стержней в спецификации ориентировочные и уточняются после контрольного обмера проёма.

УЗЕЛ С1. ВНУТРЕННЯЯ СКЛАДКА

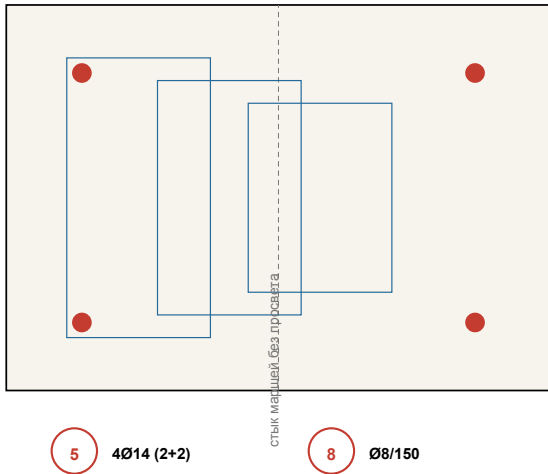

ВЕДОМОСТЬ ДЕТАЛЕЙ АРМАТУРЫ			
Поз.	Эскиз и размеры, мм	Марка	Назначение
1		Ø14 А500С	нижняя рабочая маршей
2		Ø12 А500С	верхняя в опорах/повороте
3		Ø8 А500С	поперечная распределительная
4		Ø10 А500С	радиальная забежной зоны
5		Ø14 А500С	стержни внутренней складки
6		Ø14 А500С	свободные наружные кромки
7		Ø8 А500С	П-хомуты кромок
8		Ø8 А500С	заминутые хомуты складки
9		Ø14 А500С	анкеровка в опорах

СПЕЦИФИКАЦИЯ АРМАТУРЫ (ОРИЕНТИРОВОЧНО)						
Поз.	Наименование	Кол.	L, мм	кг/м	Масса, кг	Прим.
1	Ø14 А500С	16	4200	1,210	81,3	2 марша
2	Ø12 А500С	16	2200	0,888	31,3	верх
3	Ø8 А500С	56	950	0,395	21,0	2 слоя
4	Ø10 А500С	14	1900	0,617	16,4	средн.
5	Ø14 А500С	4	3300	1,210	16,0	складка
6	Ø14 А500С	8	3600	1,210	34,8	кромки
7	Ø8 А500С	30	850	0,395	10,1	П-хом.
8	Ø8 А500С	20	900	0,395	7,1	хомут
9	Ø14 А500С	8	1500	1,210	14,5	анеры
Итого арматуры: около 233 кг		Бетон В25: около 1,5 м³			Уточнить по месту	

Монолитная П-образная лестница. Армирование

Проем 2100 x 2700; Н=2950; 18 подъёмов; марши 1050 мм

Предварительная схема КЖ-Э. По структуре предоставленного фото-чертежа.

Перед изготовлением каркаса выполнить контрольный обмер и расчёт конструктором.

Стадия КЖ-Э Лист 1 Листов 1

Масштаб 1:20 / узлы 1:10

Дата 06.09.2026 Лестница Лм-1

НЕ ДЛЯ БЕТОНИРОВАНИЯ БЕЗ ПОДПИСИ ГИП/КОНСТРУКТОРА